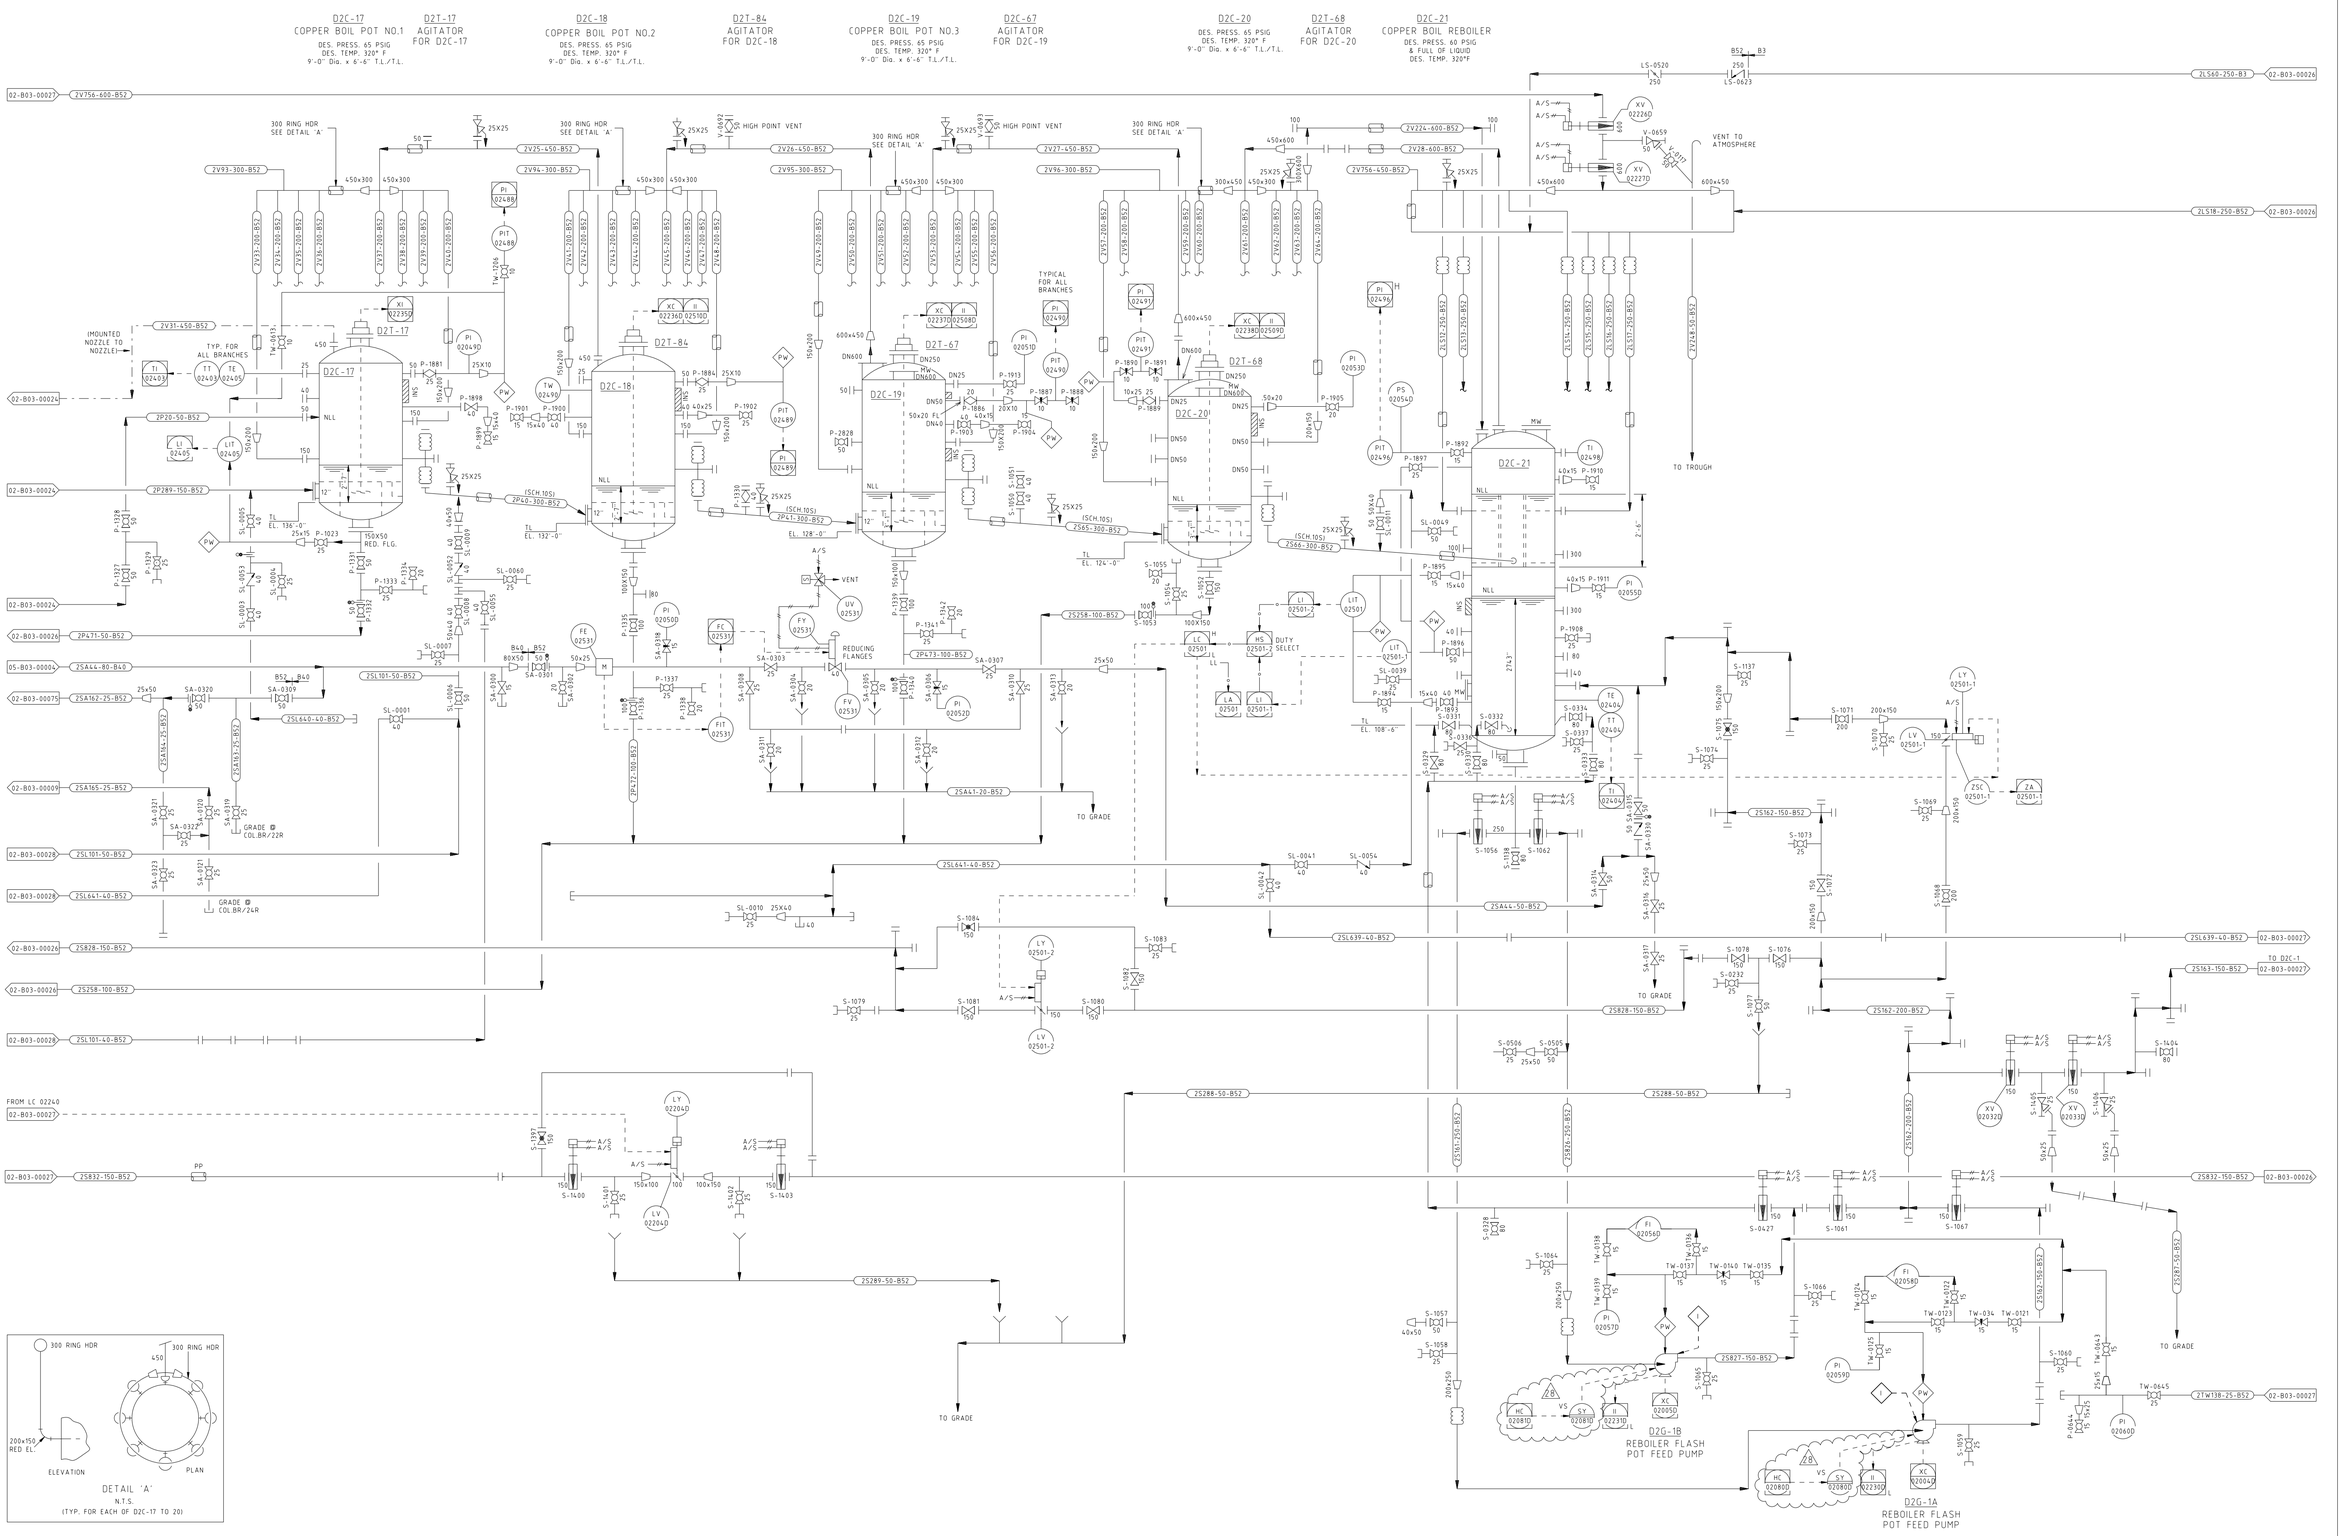

REVISIONS	No	DATE	DRN	CHK	ENG	APP	REVISIONS	No	DATE	DRN	CHK	ENG	APP	REFERENCE DRAWINGS	NUMBER	REFERENCE DRAWINGS	NUMBER
AS BUILT FOR MOC 13/064	27	10.06.16	MJP	SMP	BM	RJ	PI02488 MOVED TO DWG. 05-B03-00015 - AS BUILT	22	23.11.10	MJP	DMA	LO'C	LB				
SULPHUR LINE ADDED AS BUILT	26	21.11.13	POL	MJP	LA	MP	VALVE S-1737 REMOVED. AS BUILT 00/00059 2 EXPANSION JOINTS REMOVED - AS BUILT	21	01.09.10	CMP MJP	POL	BJ	LB				
AS BUILT FOR PROJECT S500.C.20862 & MOC 13/010	25	20.03.12	DMA	MJP	LA BS	BK	VALVE V-0117 ADDED TO LINE 2V756-600-B52	20	30.05.08	MJP	DMA	SD	NM				
NON RETURN VALVE RELOCATED AS BUILT	24	6.7.11	POL	CB	AS	CS											
SITE CHECKED & AS BUILT	23	16.06.11	IMP	DMA	MC	LB	AS BUILT S500.C.21067.1400	28	17.10.16	MO	SMP	MM	RJ			COPPER BOIL - PEFS	02-B02-0012

BHP

SCALE	N.T.S.	DATE
DRAWN	SLATER GAP	7.6.06
CHECKED	DR	7.6.06
ENGINEER		
APPROVED		

AREA 2
COPPER BOIL - SHEET 3

PIPING AND INSTRUMENTATION DIAGRAM

NICKEL WEST KWINANA NICKEL REFINERY
ABN 76 004 184 598

NUMBER: 02-B03-00025

REV: 28 | A0