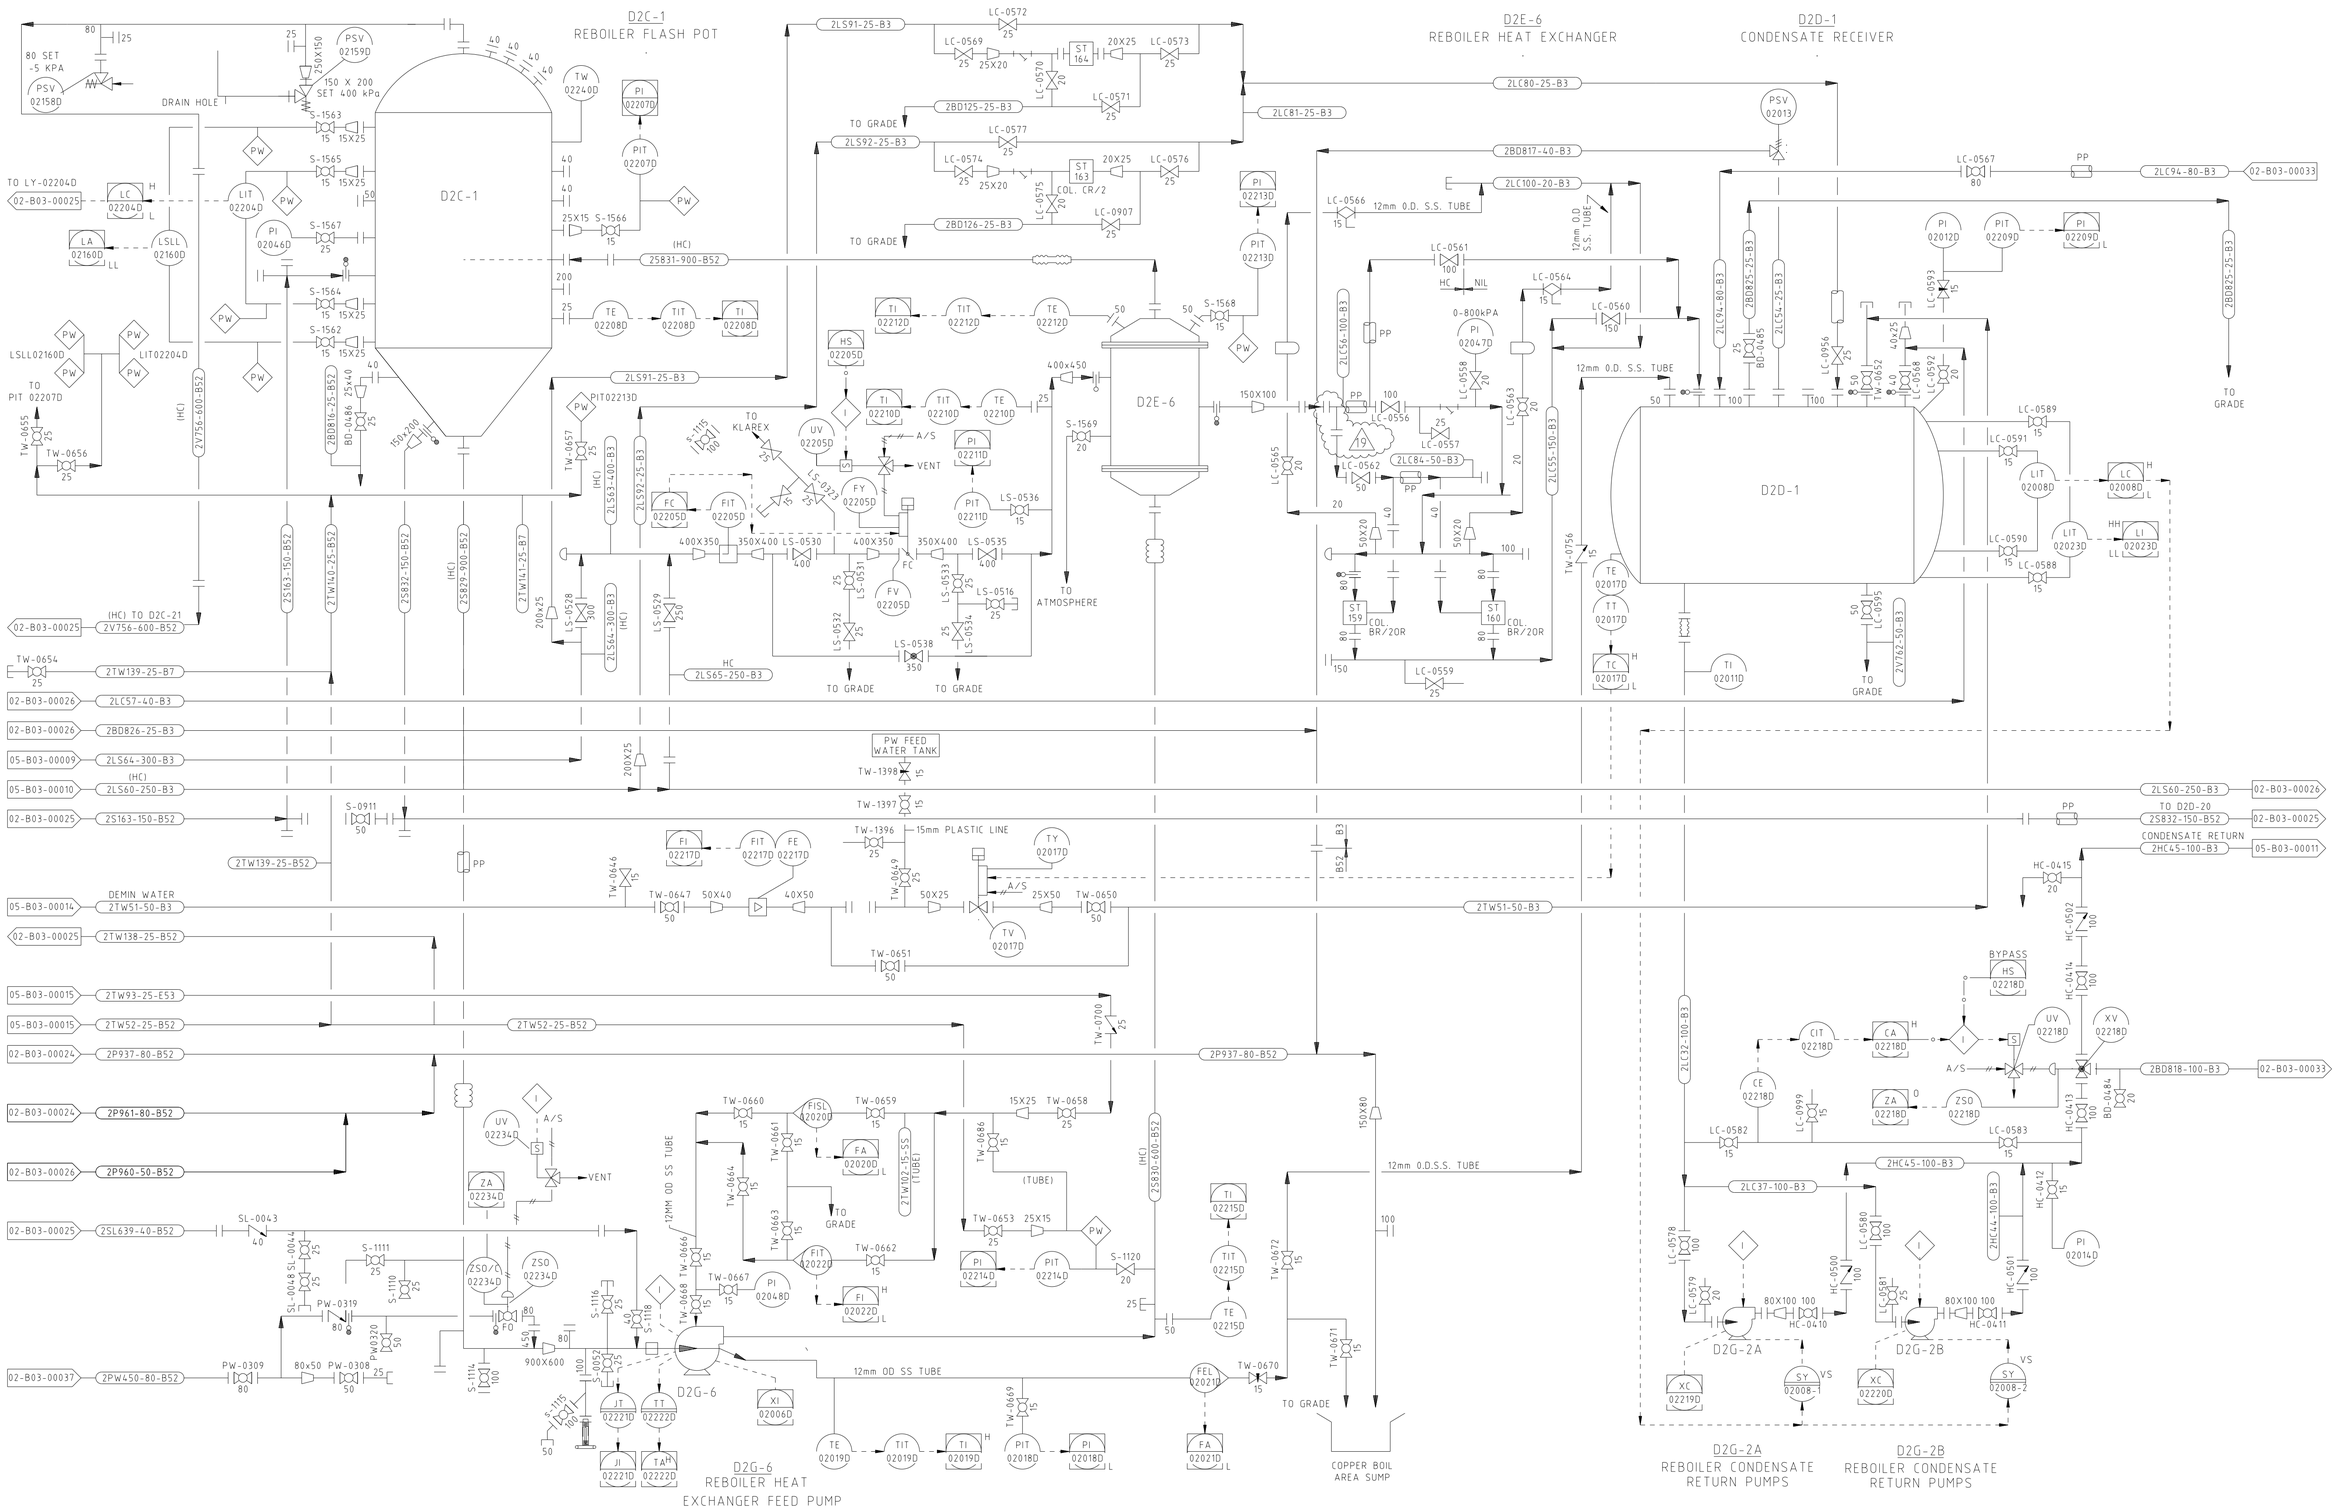

REVISIONS	No	DATE	DRN	CHK	ENG	APP	REVISIONS	No	DATE	DRN	CHK	ENG	APP	REFERENCE DRAWINGS	NUMBER
REVISED FOR PLANT MOD 03/032 VALVE LS-0516 & DN80 STUB ADDED.	15	05.06.08	DA	SPO	SD	NM									
UPDATE P&ID PIPE DN40 TO DN80 #5750.C.200094	14	13.12.07	AS	POL	CD	NM	FLANGES ADDED AS BUILT	19	13.3.12	POL	DMA	BC	BK		
PSV02158D & PSV02159D ADDED - AS BUILT	13	28.03.07	SPo	POL	NQ	AL	STEAM TRAPS UPDATED AS BUILT VALVE S-1112 REMOVED	18	01.03.12	CB	POL	SD BK	BK		
LINE DGN NUMBER REVISED "AS BUILD"	12	28.06.06	JM	BG	BG	GP	SITE CHECKED AND AS BUILT	17	04.04.11	IMP	DMA	KH	LB	COPPER BOIL - PEFS	02-B02-00012
LINE 2PW450-80-B52 AS BUILT	11	24.01.06	MHC	GS	MD	GP	VALVES TO KLAREX ADDED. 5750.0.20375	16	03.09.08	CMP	SPo	EK	CS	COPPER BOIL CONDENSATE - PEFS	02-B02-00010

BHP

SCALE	N.T.S.	DATE
DRAWN	MC	29.8.95
CHECKED	AJS	25.09.96
ENGINEER		
APPROVED		

××WORK IN PROGRESS××AREA 2
COPPER BOIL INDIRECT HEATING

PIPING AND INSTRUMENTATION DIAGRAM

NICKEL WEST KWINANA NICKEL REFINERY ABN 76 004 184 598

NUMBER
02-B03-00027

REV: 19 | A1